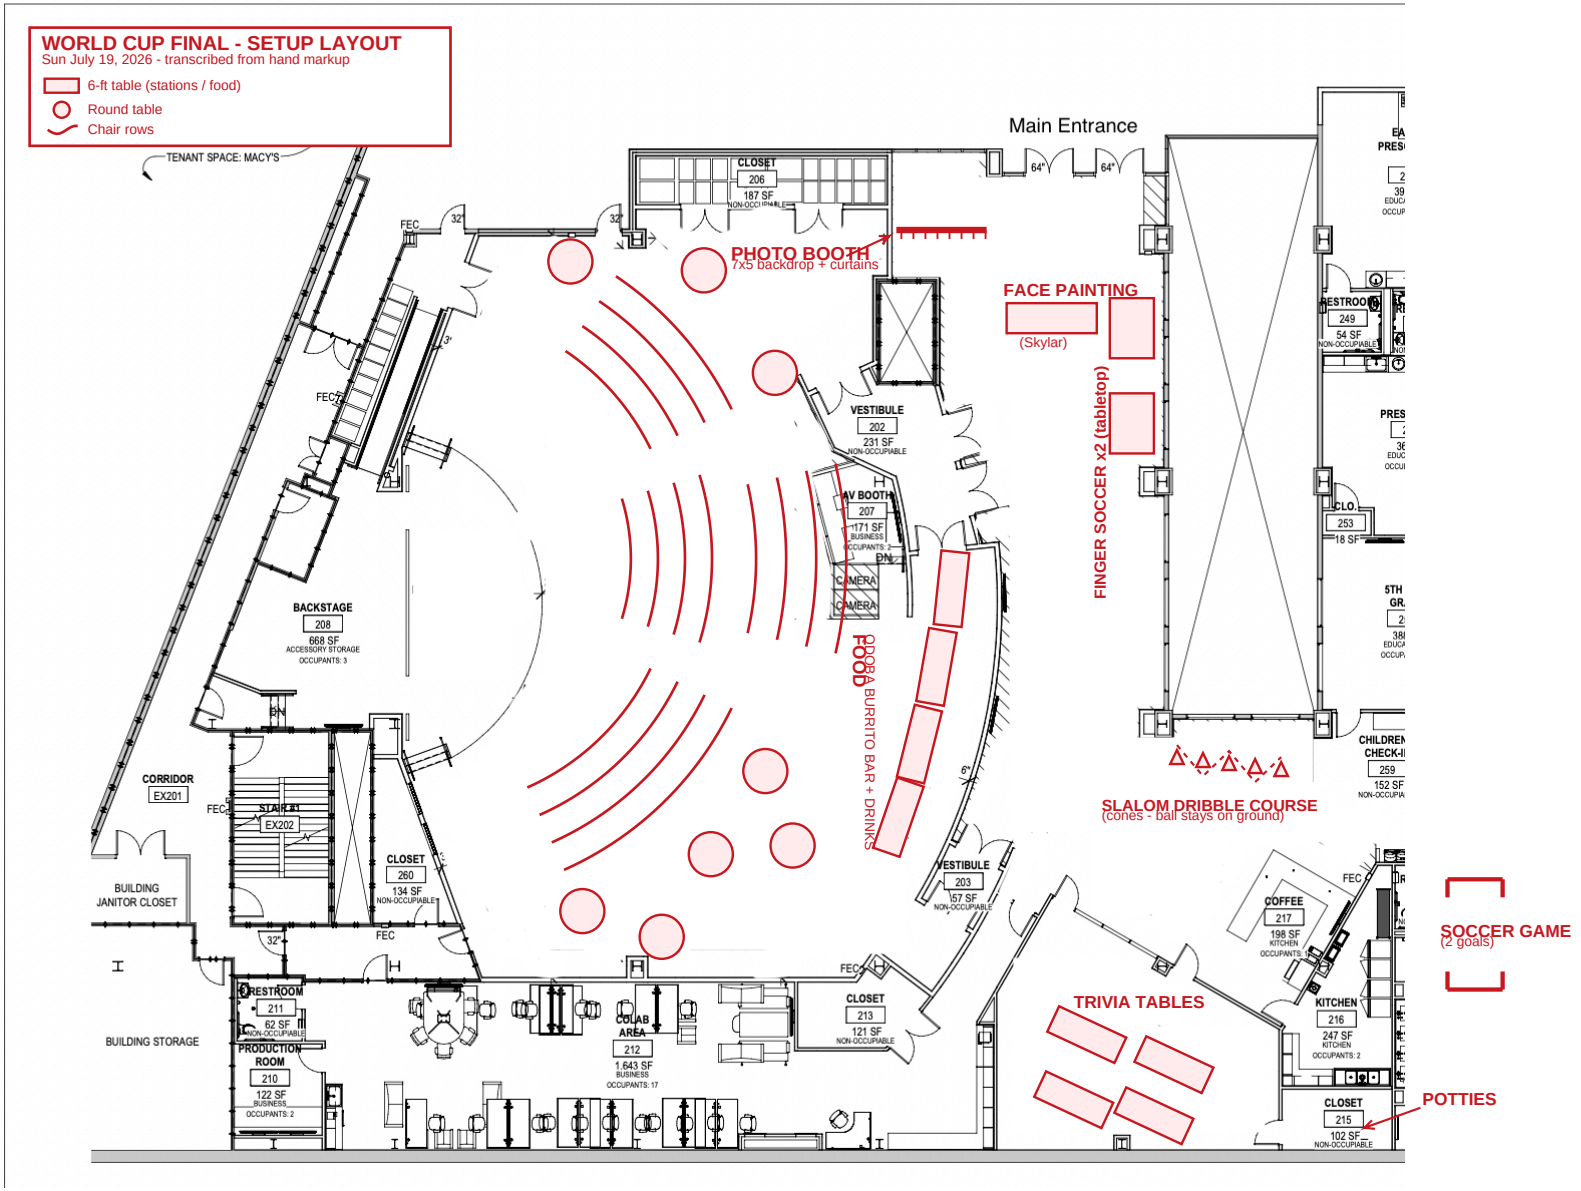

WORLD CUP FINAL - SETUP LAYOUT
Sun July 19, 2026 - transcribed from hand markup
6-ft table (stations / food)
Round table
Chair rows
Main Entrance
TENANT SPACE: MACY'S
CLOSET 206 187 SF NON-OCCUPIABLE
PHOTO BOOTH
7x5 backdrop + curtains
FACE PAINTING
(Skylar)
FINGER SOCCER x2 (tabletop)
VESTIBULE 202 231 SF NON-OCCUPIABLE
AV BOOTH 207 171 SF BUSINESS OCCUPANTS: 2
CAMERA
CAMERA
BACKSTAGE 208 668 SF ACCESSORY STORAGE OCCUPANTS: 3
FOOD
CHIPOTLE BURRITO BAR + DRINKS
RESTROOM 249 54 SF NON-OCCUPIABLE
CLO 253 18 SF
CHILDREN CHECK-I 259 152 SF NON-OCCUPIA
SLALOM DRIBBLE COURSE
(cones - ball stays on ground)
CORRIDOR EX201
STAIR #1 EX202
CLOSET 260 134 SF NON-OCCUPIABLE
BUILDING JANITOR CLOSET
VESTIBULE 203 157 SF NON-OCCUPIABLE
COFFEE 217 198 SF KITCHEN OCCUPANTS: 1
SOCCER GAME
(2 goals)
RESTROOM 211 62 SF NON-OCCUPIABLE
BUILDING STORAGE
PRODUCTION ROOM 210 122 SF BUSINESS OCCUPANTS: 2
COLAB AREA 212 1,643 SF BUSINESS OCCUPANTS: 17
CLOSET 213 121 SF NON-OCCUPIABLE
TRIVIA TABLES
KITCHEN 216 247 SF KITCHEN OCCUPANTS: 2
CLOSET 215 102 SF NON-OCCUPIABLE
POTTIES